



DISPOSICION GENERAL POSTE DE 11,5 METROS CARA A
ESCALA 1 : 20

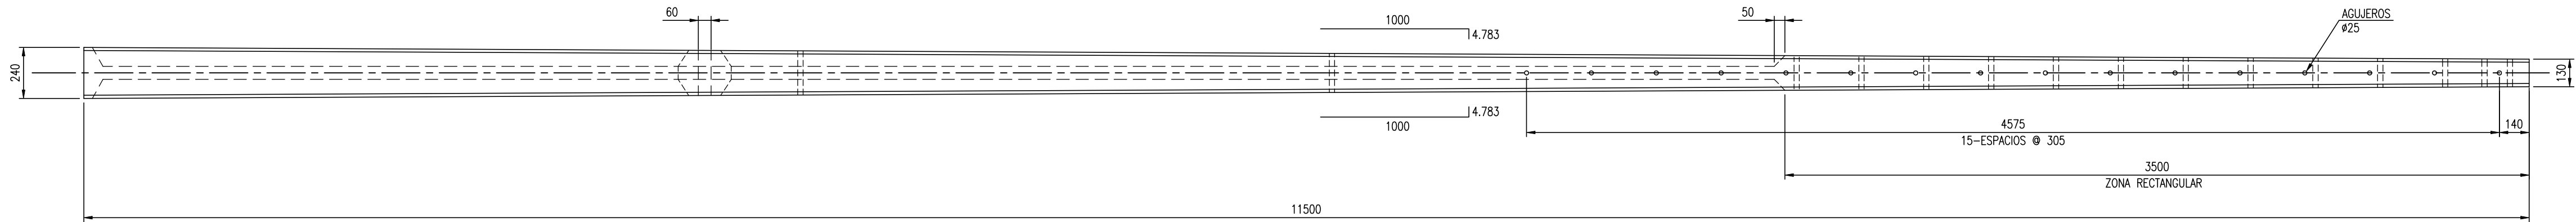

DISPOSICION GENERAL POSTE DE 11,5 METROS CARA B
ESCALA 1 : 20

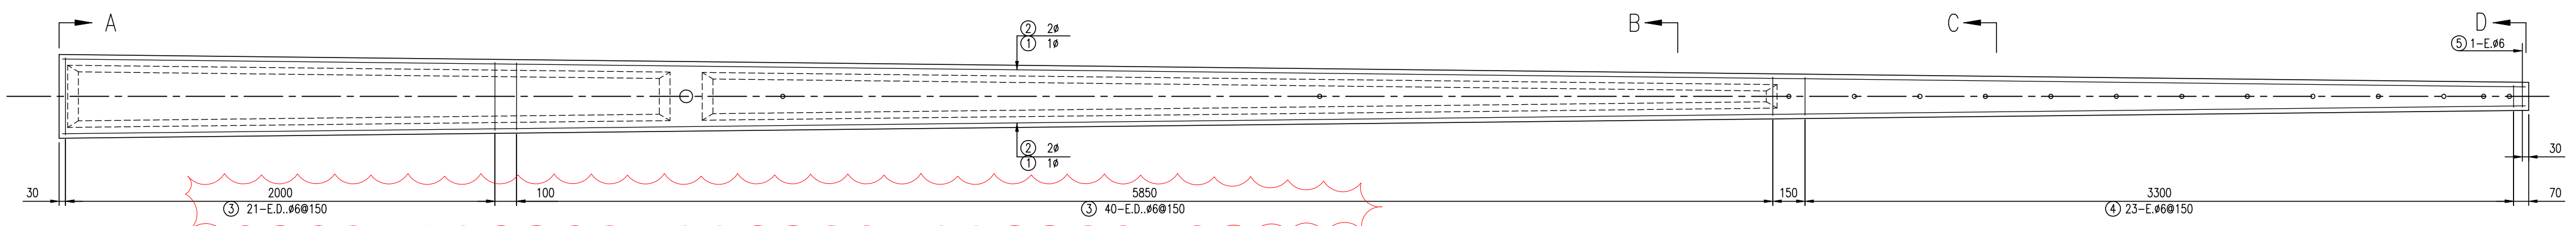

DISPOSICION DE ARMADURAS POSTE DE 11,5 METROS
ESCALA 1 : 20




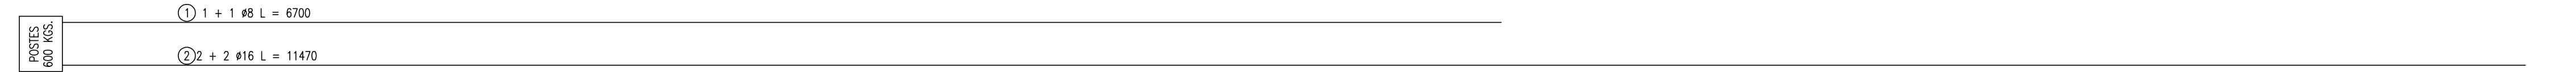



DIAGRAMA DE MONTAJES

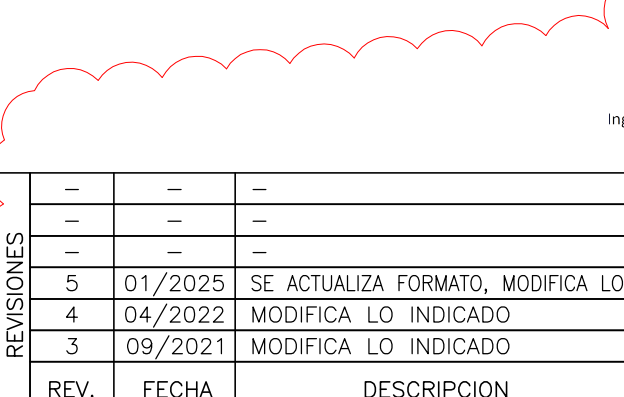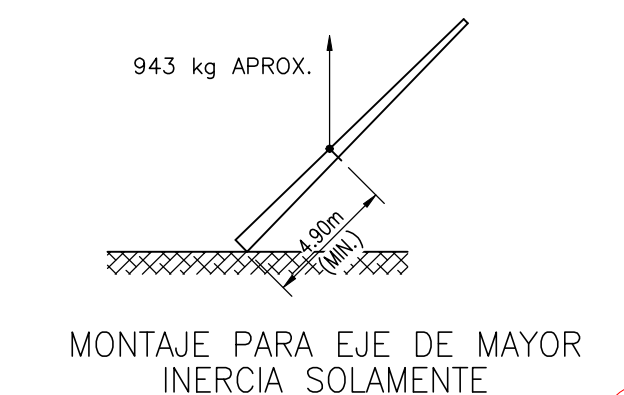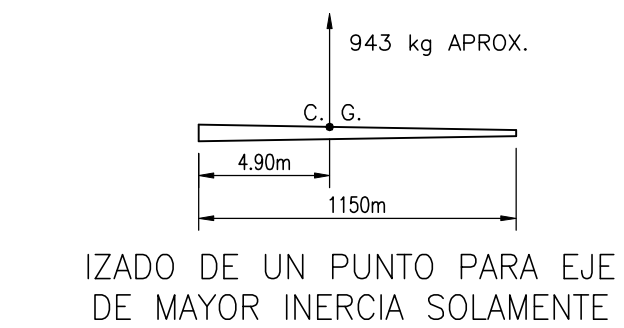

CUBICACIÓN ARMADURAS PARA POSTE 11,50m

N°	CANT.	TIPO	Ø	DIMENSIONES PARCIALES				LARGO TOTAL m.	RESUMEN DE FIERRO
				A	B	C	D		
1	2	1	8	6700				13.40	#8 = 5.29 KG.
2	4	1	16	11470				45.88	#16 = 72.49 KG.
3	122	2	6	81	101	101	50	LW 0.57	#6 = 18.7 KG.
4	23	3	6	101	101	101	50	LW 0.61	
5	1	3	6	100	100	50		0.50	TOTAL = 96.5 KG.

HORMIGON C25 0.377m³
PESO APROX. DE UN POSTE EN KG.
PARA 600 KG. 943

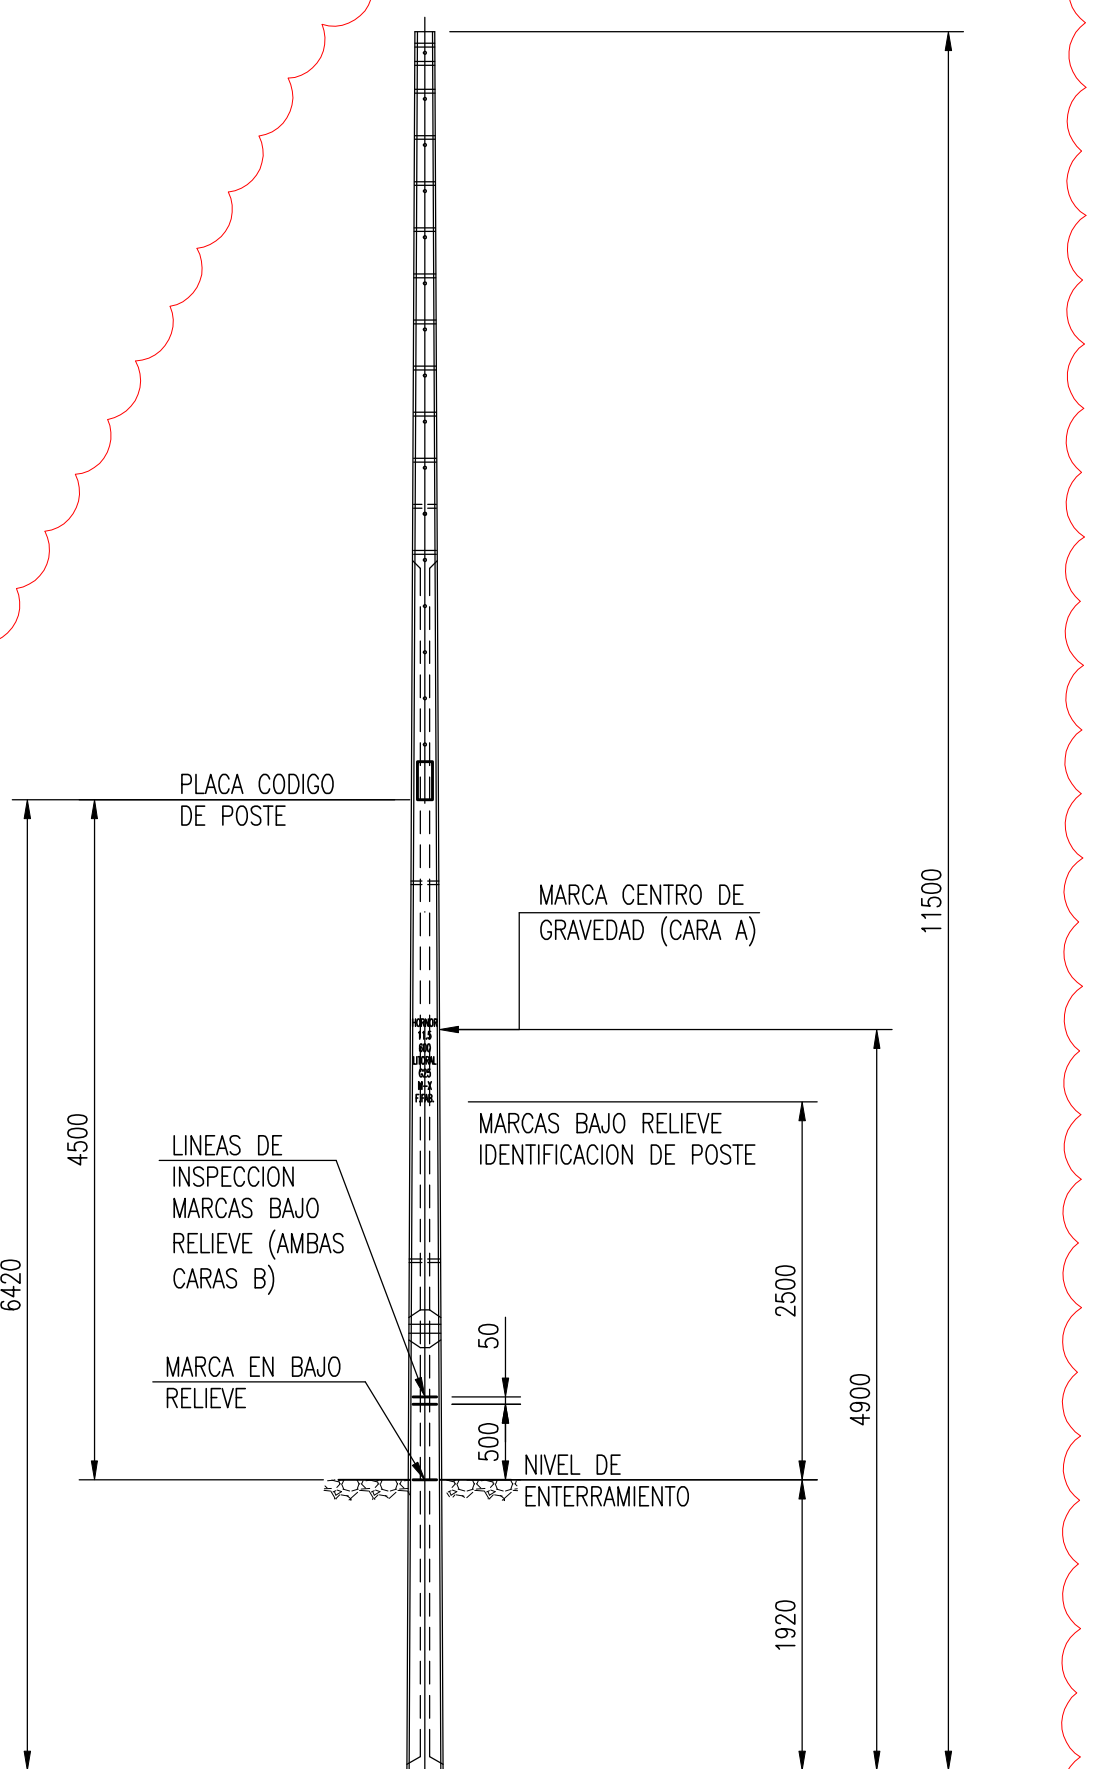


MARCADO DEL POSTE (CARA B)
Escala 1:50

NOTAS

- TODAS LAS DIMENSIONES EN mm, S.I.C.
- ACERO ARMADURAS SEGUN Nch 204
 - CALIDAD A630-420H CON RESALTES PARA, #8 A 22 mm
 - CALIDAD A440-280H PARA #6 mm
- ARMADURAS SEGUN Nch 211
 - RECUBRIMIENTO MINIMO DE ARMADURAS: 20 mm
 - DIMENSIONES INDICADAS EN CUADRO DE ARMADURAS SON EXTERIORES
- HORMIGON: C25 SEGUN Nch 170, CON FRACCION DEFECTUOSA MAX. 5%
TAMANO MAXIMO DEL AGREGADO GRUESO 3/4"
- TODOS LOS AGUJEROS SON #25mm

CARGA DE SERVICIO
EQUIVALENTE EN LA PUNTA

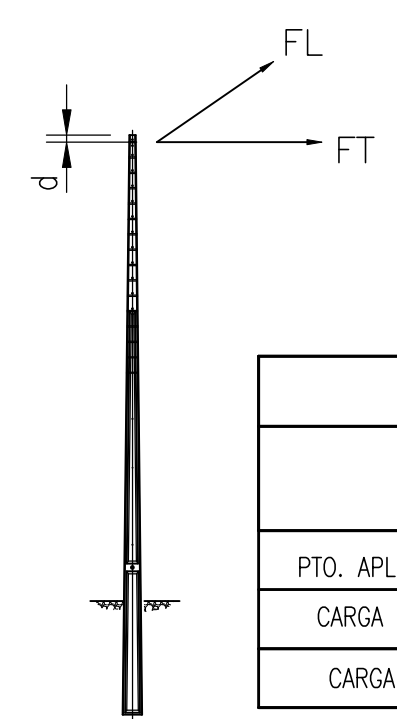

	ESFUERZOS kg	
	FT (FLECTA EJE FUERTE)	FL (FLECTA EJE DEBIL)
PTO. APLICACION (d)	140 mm	90 mm
CARGA ADMISIBLE	300	75
CARGA ROTURA	600	150

SIMBOLOGIA
E.: ESTRIBO
E.D.: ESTRIBO DOBLE
Tr.: TRABA
B.: BARRA
@: "A" (SEPARACION ENTRE BARRAS)
ELEV.: ELEVACION
VAR.: VARIABLE

TITULO		POSTE DE HORMIGON ARMADO L=11.5m	
TIPO		SAESA	
CARGA DE SERVICIO P=300kg / CARGA DE ROTURA Fu=600kg			
CONTENIDO		FORMA Y DIMENSIONES ARMADURAS CUADRO DE CARGAS, NOTAS	
CALCULO	GGG	CODIGO PRODUCTO	11804
REVISO		LAMINA N°	HN-11804-PL-01
DIBUJO	JVP/RCS	FECHA	05/11/2018
		ESCALAS	INDICADAS
		REVISION	5